
# ПЛАН ШОКОЛАДНОГО ЦЕХА

40 x 24 м · А0 · Масштаб 1:50

Прямые вызовы API v21: оборудование, санитарные приборы, маршруты и нативные размеры

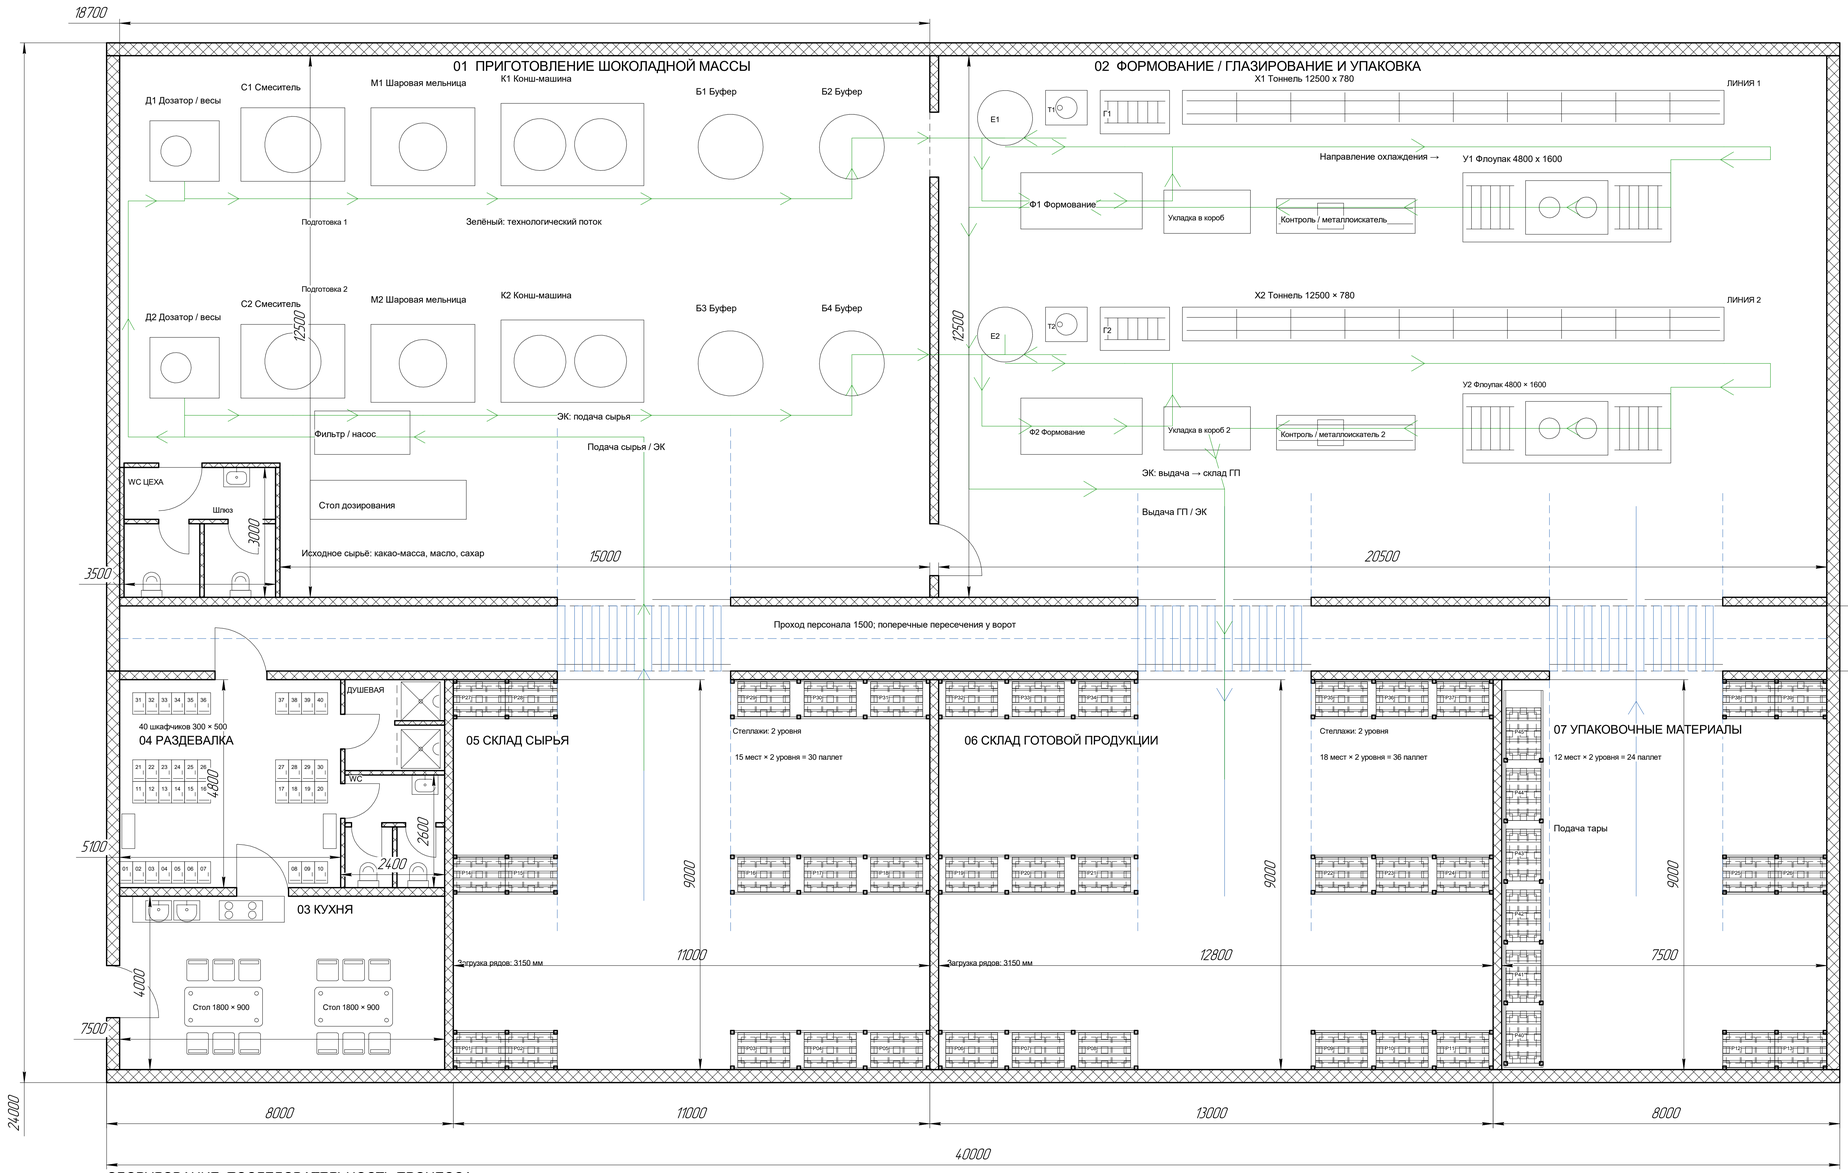


## ЭКСПЛИКАЦИЯ

01 Приготовление шоколадной массы

02 Формование / глазирование, упаковка

03 Кухня / отдых

04 Раздевалка; WC и душевые

05 Склад сырья

06 Склад готовой продукции

07 Склад упаковочных материалов

08 Проход персонала 1.5 м; пересечения ЭК

09 WC цеха; вход через шлюз

## МАРШРУТЫ

Продукция / шоколадная масса

Маршрут электрокара

Склады соединены с цехами

через встречные ворота 4 м.

Зелёные линии между машинами:

трубопровод / конвейер / перегрузка.

Сырьё: готовые какао-продукты.


Измельчение и конширование — цех 01.

Размеры указаны в мм.

WC, душ, мойка — контуры с дугами,

сливами и обозначением прибора.

Стеллаж: 3 секции, 2 уровня

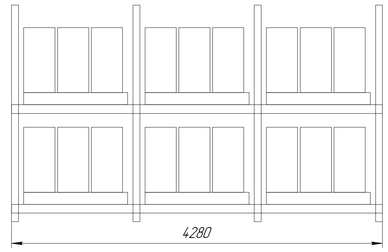


## ОБОРУДОВАНИЕ: ПОСЛЕДОВАТЕЛЬНОСТЬ ПРОЦЕССА

Д1 Дозирование → С1 Смешивание → М1 Измельчение → К1 Конширование → Б1/Б2 Буфер

Е1 Ёмкость Ø1270 → Т1 Темпер 960 x 800 → Г1 Глазировка 1600 x 1000 → Х1 Тоннель 12500 x 780

Две параллельные линии: глазирование / формование → охлаждение → флоупак → контроль → склад ГП

Охлаждающий тоннель сохранён: 12500 x 780 мм, высота H=1530 мм.

Технология: Bühler (DoMiReCo / SmartChoc), SOLLICH (tempering, enrobing, cooling).

Габариты дополнительного оборудования — компоновочные допущения, без выбора конкретной модели.

Учебный пример API. Манёвры ЭК и нормативная планировка требуют отдельного проектного расчёта.

Шоколадный цех — план

Редакция 7 / 2 подготовки + 2 линии

| Изм. | Лист | № докум. | Подп. | Дата | Лит. | Масса | Масштаб |
|---|---|---|---|---|---|---|---|
| Разраб. | | | | | | | 150 |
| Пров. | | | | | | | |
| Т.контр. | | | | | Лист | Листов 1 | |
| Н.контр. | | | | | | | |
| Утв. | | | | | | | |

Копировал Формат А0

Перв. примен. | Справ. № | Подп. и дата | Инв. № подл. | Взам. инв. № | Инв. № дубл. | Подп. и дата